
PF257

PORTA METÁLICA DE ABRIR + GRADE + VENEZIANA + POLICARBONATO 4mm


DIM.: 200x240cm

ESPECIFICAÇÕES:
01 - MARCO / BATENTE EM CHAPA FINA A FRIO, DE AÇO DOBRADA. CHAPA 16" =1,50mm;
02 - MOLDURA EM CHAPA FINA A FRIO, DE AÇO DOBRADA. CHAPA 16" =1,50mm;
03 - DOBRADIÇA TIPO CACHIMBO EM AÇO TORNEADO;
04 - TRANCA TIPO FERROLHO - colocar no lado interno do controle (VER DETALHE);
05 - VENEZIANA EM CHAPA 16" DE AÇO DOBRADA;
06 - POLICARBONATO CRISTAL 4mm;
07 - BARRA REDONDA DE AÇO ∅1/2";
08 - CANTONEIRA DE AÇO 5/8"x1/8";
09 - BARRA CHATA DE AÇO 2"x1/8";
10 - REFORÇO EM BARRA CHATA DE AÇO 1"x1/8";
11 - FECHADURA IMAB MODELO DUNA 2, ZAMAC CROMADO. CÓDIGO CJ1577E17CR DUNA 2 CR.;
12 - REQUADRO INTERNO NA FOLHA COM BARRA CHATA DE 1.1/2"x1/8";
13 - REFORÇO INTERNO DA VENEZIANA COM BARRA CHATA DE AÇO 2"x1/8";
14 - CANTONEIRA PARA TRAVAMENTO EM AÇO 4"x3/8";
15 - ALÇA DO PERFIL DE TRAVAMENTO.


OBSERVAÇÕES:
-O POLICARBONATO SERÁ INSTALADO NA PARTE INTERNA;
-A BARRA CHATA SERÁ PREVIAMENTE SOLDADA NAS BARRAS REDONDAS;
-AS BARRAS REDONDAS SERÃO SOLDADAS NA CHAPA QUE COMPÕEM A FOLHA DA PORTA;
-A CANTONEIRA SERÁ FIXADA NA FOLHA POR MEIO DE REBITES (ESPAÇAMENTO DE 10cm);
-PREVER ACABAMENTO ANTIFERRUGINOSO;
-A TRANCA TIPO FERROLHO E O VIDRO LAMINADO SERÁ INSTALADO NO LADO INTERNO DO AMBIENTE (CONTROLE AGENTE);
-VERIFICAR SENTIDO DE ABERTURA DA PORTA NO PROJETO ARQUITETÔNICO;
-PREVER PINTURA NAS CHAPAS TAMBÉM NO LADO INTERNO;
-MEDIDAS EM CENTÍMETROS (cm);
-CONFERIR MEDIDAS NO LOCAL.

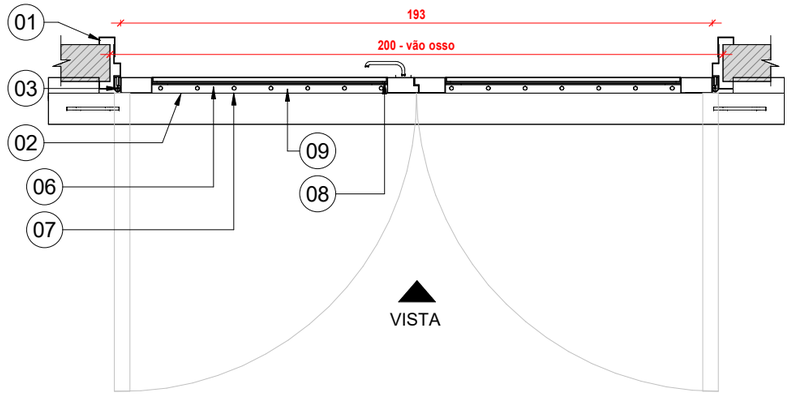


PLANTA
ESC.:1/20
OBS.: MEDIDAS EM CENTÍMETROS

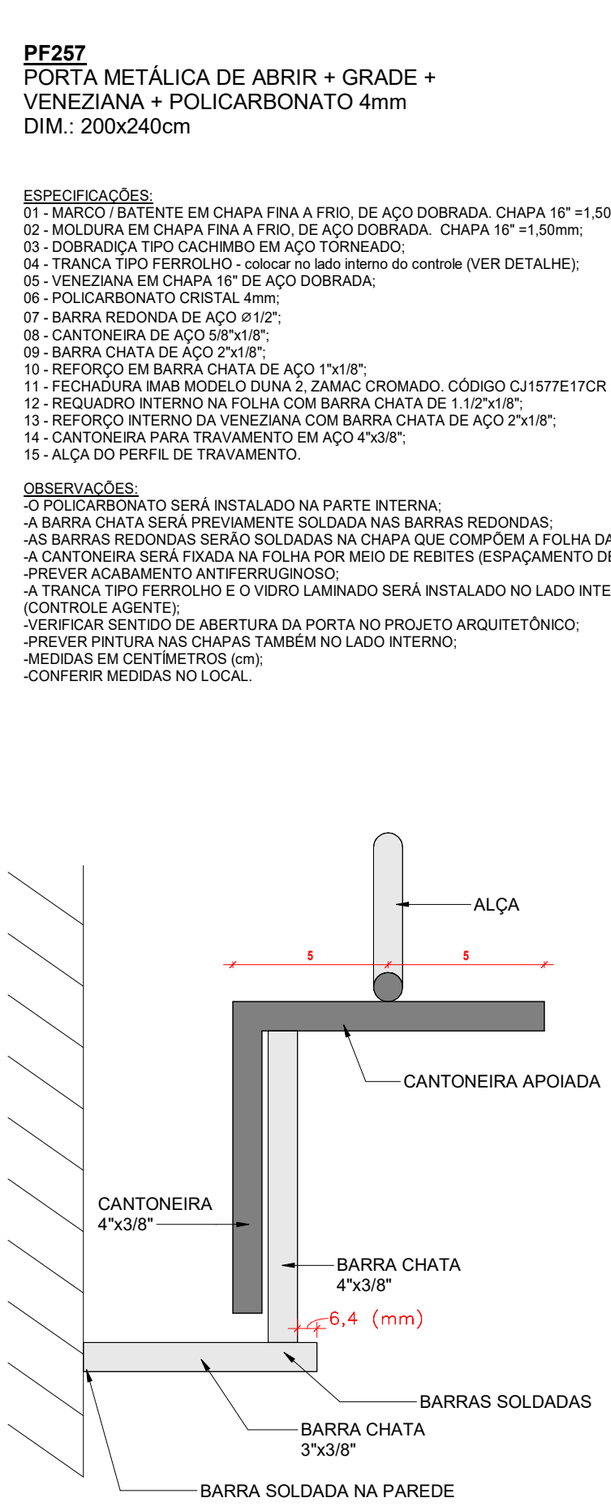

DETALHE SUPORTE (ITENS 14 E 15)
ESC.:1/2
OBS.: MEDIDAS EM MILÍMETROS

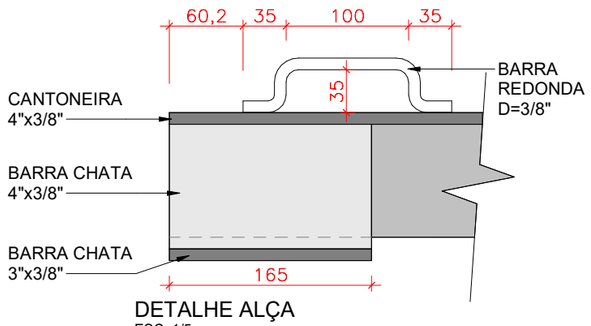

DETALHE ALÇA
ESC.:1/5
OBS.: MEDIDAS EM MILÍMETROS

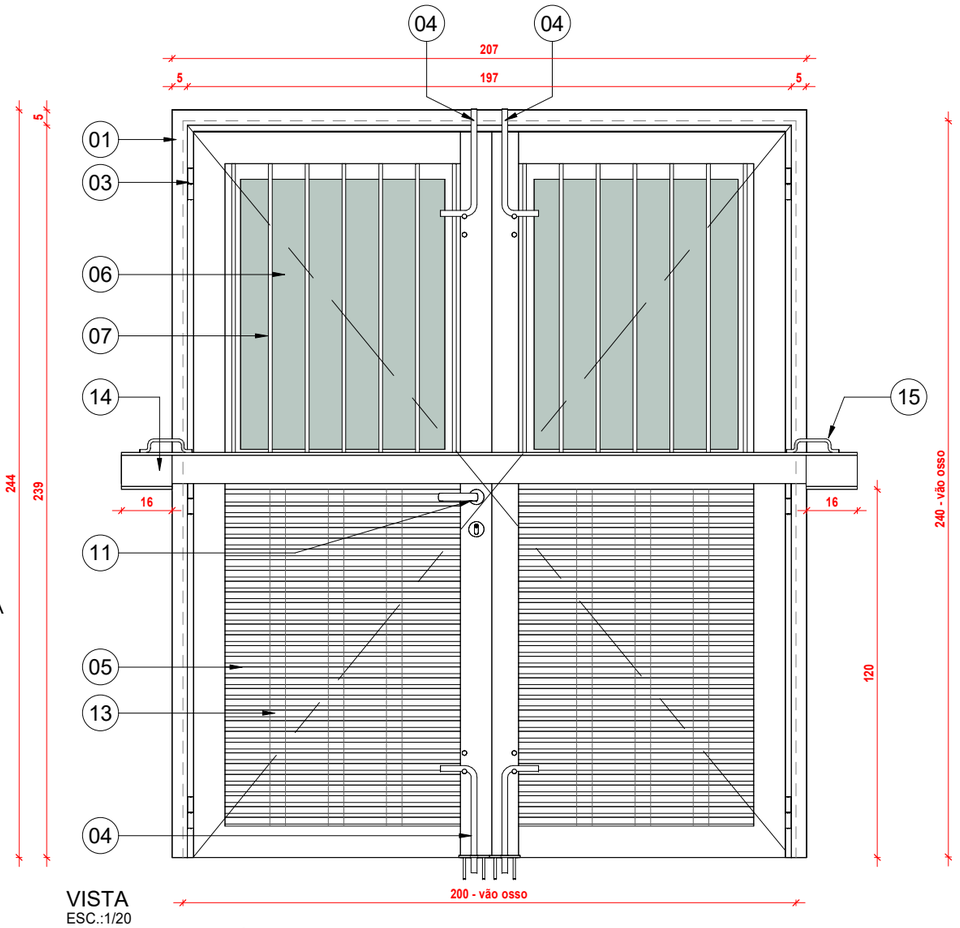

VISTA
ESC.:1/20
OBS.: MEDIDAS EM CENTÍMETROS

REV.	DATA	DESCRIÇÃO	DESENHO	APROVAÇÃO
00	18/06/2026	EMISSÃO INICIAL	A.B.	J.W.


V-SIS
Verdi Sistemas Construtivos S.A.

PROJETO: DETALHAMENTO DE ESQUADRIAS


DESCRIÇÃO: PORTA METÁLICA DE ABRIR + GRADE + VENEZIANA + POLICARBONATO 4mm

PRANCHA: PF257


DETALHE DOBRADIÇA

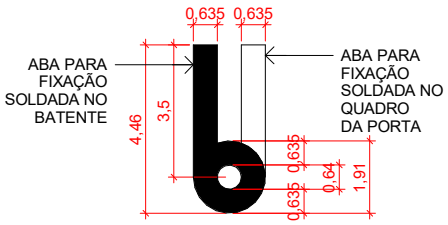


VISTA SUPERIOR
ESC.:1/2

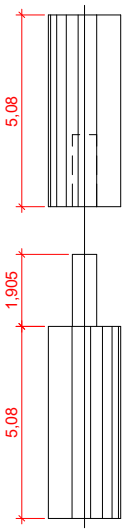


VISTA FRONTAL
ESC.:1/2

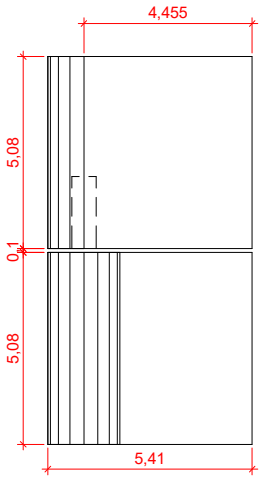

VISTA LATERAL
ESC.:1/2

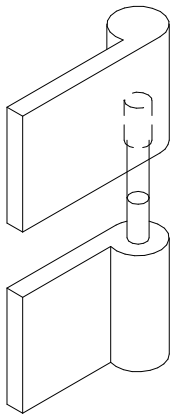



PERSPECTIVA
S/ESC.

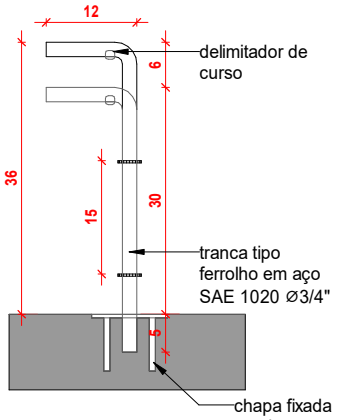


DETALHE AÇOLHO
ESC.:1/10


CHAPA FIXADA NO PISO
ESC.:1/5

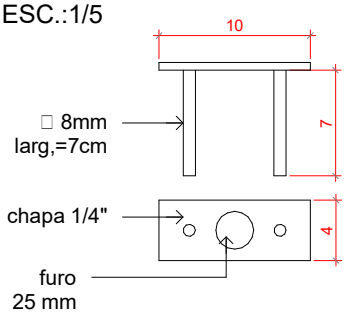

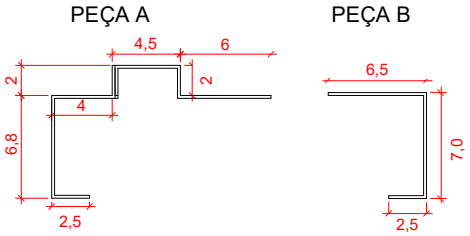

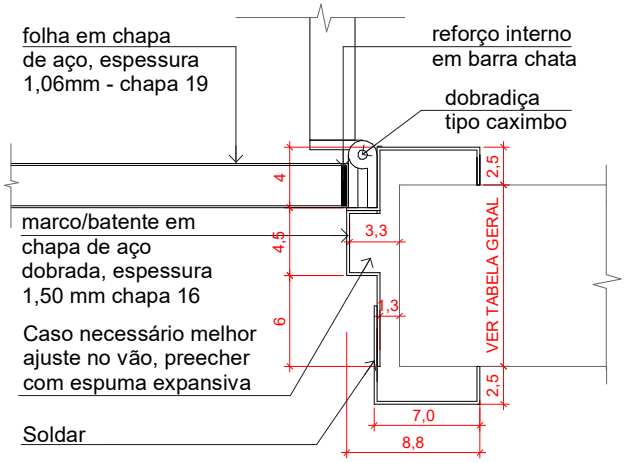

DET.MARCO
S/ESC.

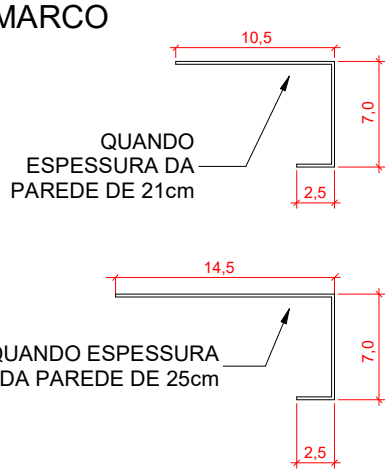

*** TODOS OS DIREITOS RESERVADOS ***

V-SIS
Verdi Sistemas Construtivos S.A.

REV.	DATA	DESCRIÇÃO
00	18/06/2026	EMISSÃO INICIAL

PROJETO: DETALHAMENTO DE ESQUADRIAS

DESCRIÇÃO: DETALHE PORTA METÁLICA DE ABRIR + GRADE + VENEZIANA + POLICARBONATO 4mm

PF257 DET. PADRÃO