POF474-e

PORTÃO METÁLICO DE CORRER EM CHAPA METÁLICA DE ACESSO DE VEÍCULOS


DIM. (OSSO): 430x500cm

ESPECIFICAÇÕES:


01 - PERFIL TUBULAR DE AÇO (PILAR/VIGA) DE SECÇÃO QUADRANGULAR 80x80mm #3,25mm;
02 - CAIXILHO EM PERFIL TUBULAR DE AÇO DE SECÇÃO RETANGULAR DE 70x30mm #3,25mm;
03 - CAIXILHO EM PERFIL TUBULAR DE AÇO #3,00mm;
04 - CHAPA CORRUGADA EM AÇO MSG 20 (#0,95mm);
05 - BATENTE EM CHAPA DOBRADA DE AÇO #3,00mm;
06 - GUIA SUPERIOR EM CHAPA DOBRADA DE AÇO #3,00mm;
07 - GUIA INFERIOR EM CHAPA DOBRADA DE AÇO #3,00mm;
08 - RODÍZIO DUPLO DE AÇO 10x3,80cm;
09 - FUROS NA CHAPA INFERIOR DOBRADA PARA ESCOAMENTO DA ÁGUA.

OBSERVAÇÕES:


- PREVER TRATAMENTO ANTIFERRUGINOSO;
- PREVER ACIONAMENTO ELETROMECÂNICO POR MOTOR;
- MEDIDAS EM CENTÍMETROS (cm);
- CONFERIR MEDIDAS NO LOCAL.

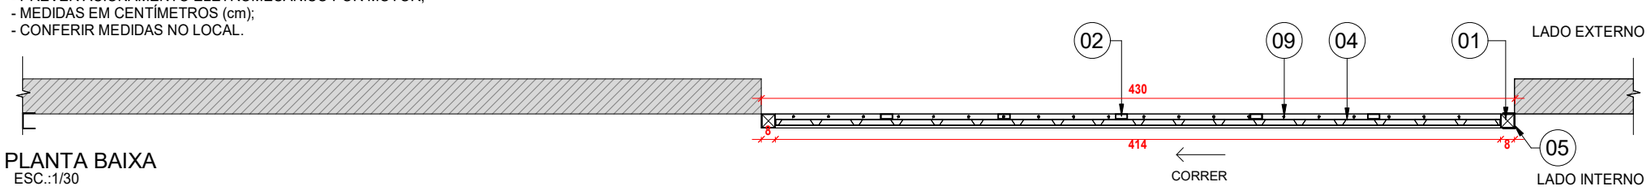

PLANTA BAIXA
ESC.:1/30

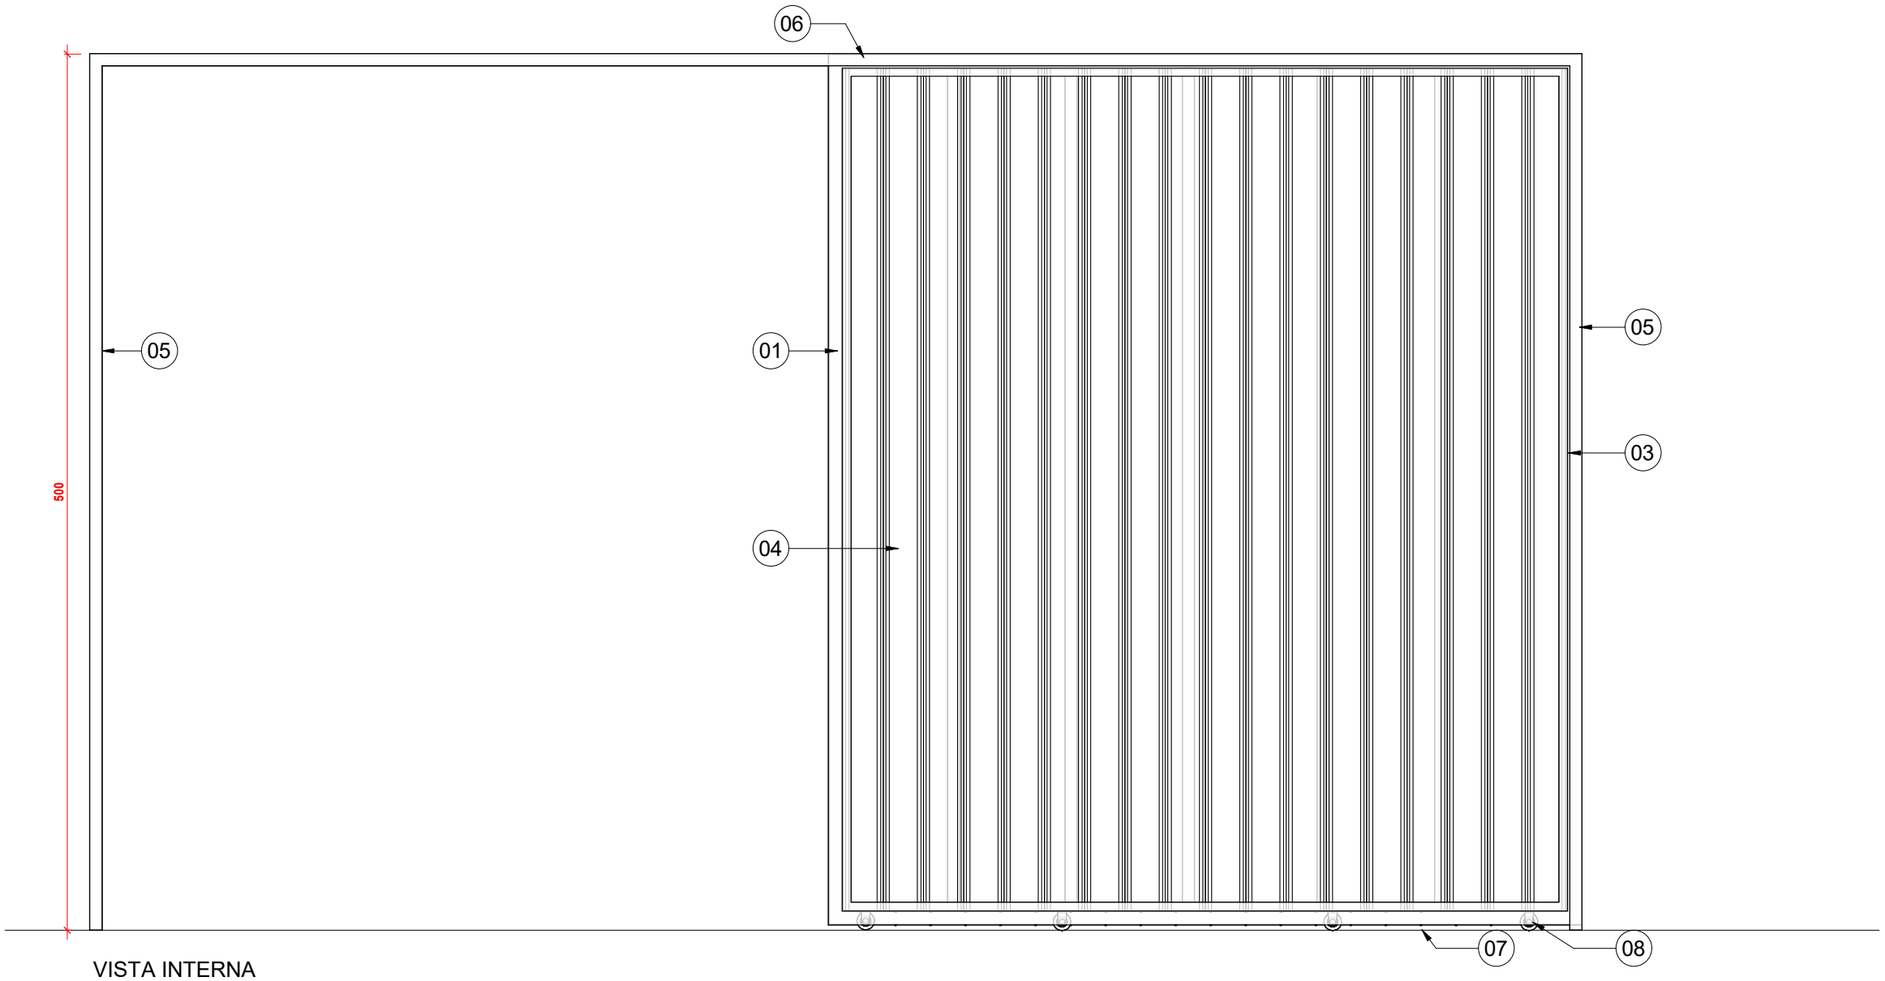

VISTA INTERNA
ESC.:1/30

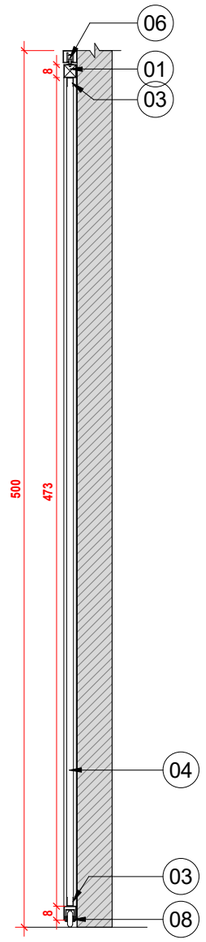

CORTE
ESC.:1/30

REV.	DATA	DESCRIÇÃO	DESENHO	APROVAÇÃO
00	18/06/2026	EMISSÃO INICIAL	A.B.	J.W.

V-SIS
Verdi Sistemas Construtivos S.A.

PROJETO: DETALHAMENTO DE ESQUADRIAS

DESCRIÇÃO: PORTÃO METÁLICO DE CORRER COM TELA DE ACESSO PARA VEÍCULOS

PRANCHA: POF474-e